





RURAL DEVELOPMENT CENTRE



Location: Shivkar, Panvel
AREA: 2100 sqm

Designed a Rural Development Centre, aimed at empowering the local community through education, skill development and social engagement. The project responds to the needs of the rural context by integrating training facilities, community spaces, administrative areas, and multifunctional activity zones. The design emphasizes sustainable planning, climate-responsive architecture, and the use of locally available materials to create an environmentally conscious and economically viable development. By fostering community participation and preserving the village's cultural identity, the proposal serves as a catalyst for rural growth, self-reliance and improved quality of life.


GROUND FLOOR PLAN

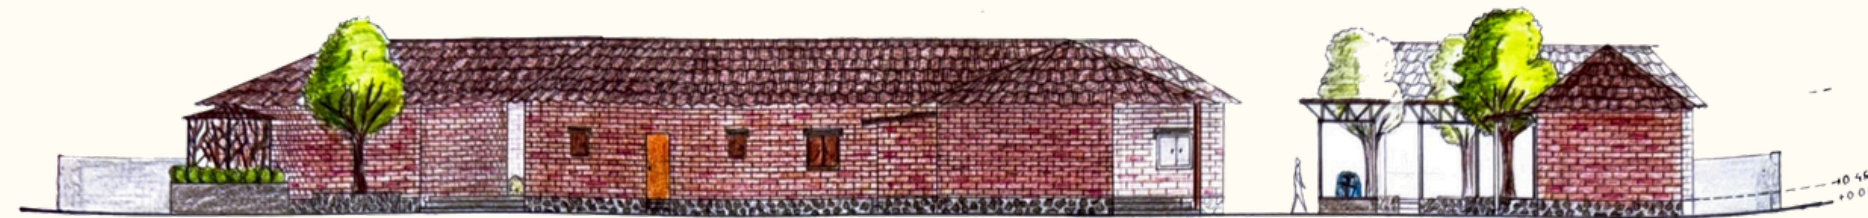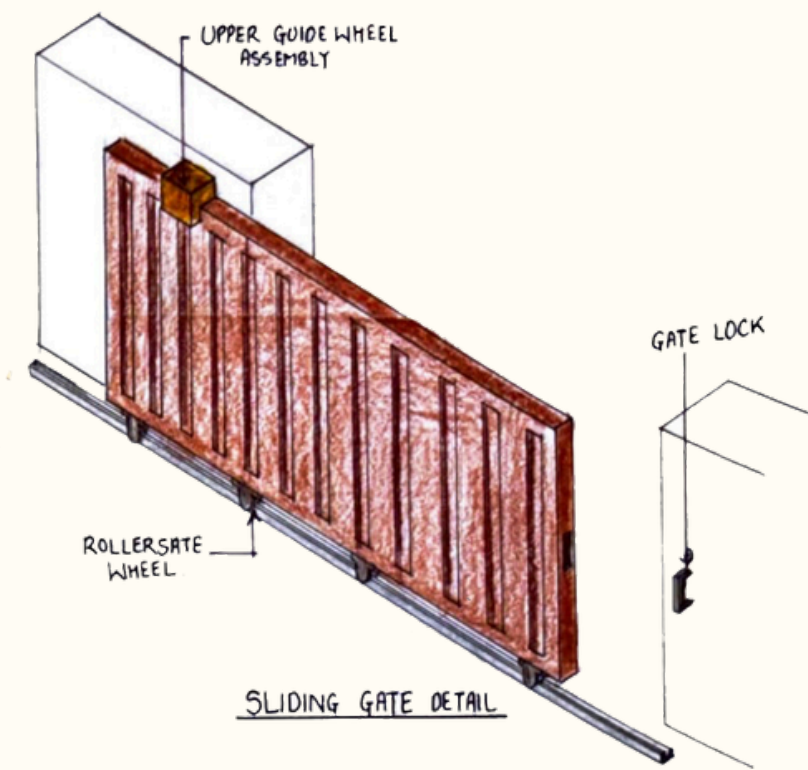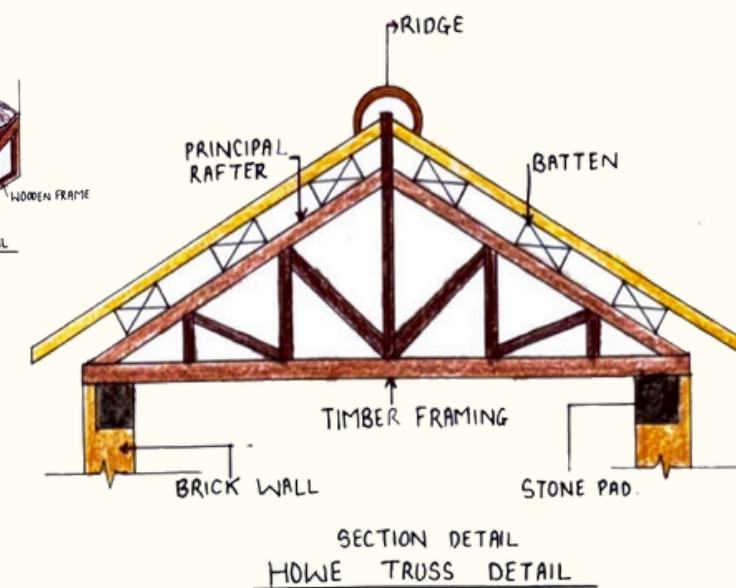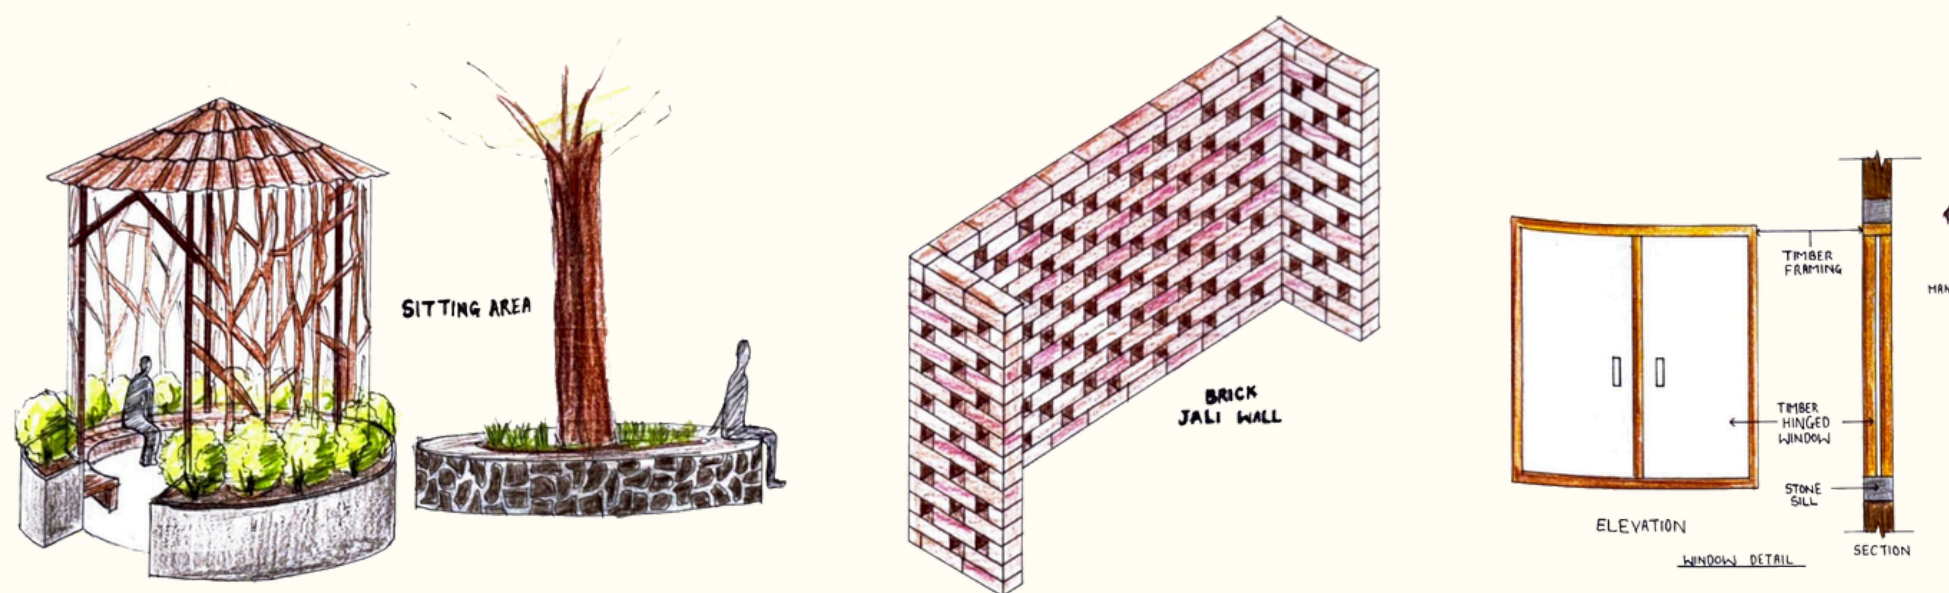

NORTH ELEVATION



WEST ELEVATION

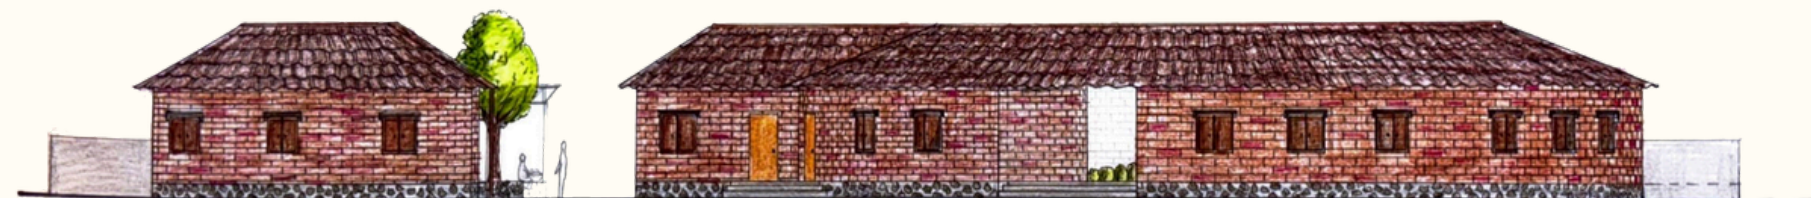


SOUTH ELEVATION



EAST ELEVATION



SECTION A-A'

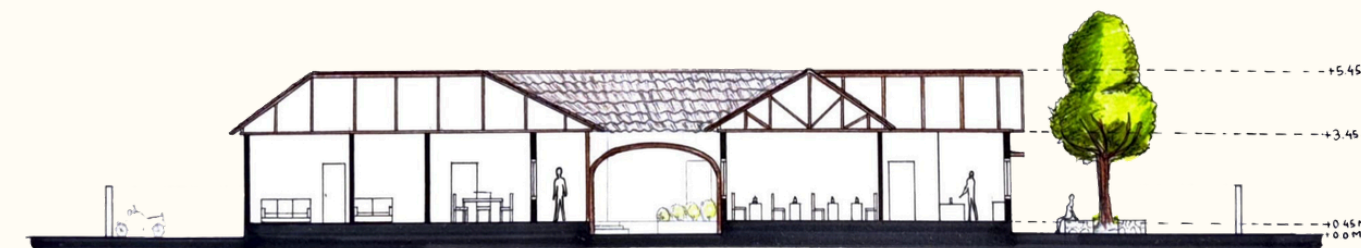

SECTION B-B'



SECTION C-C'

ELEVATIONS

SECTIONS