


WORKING DRAWINGS

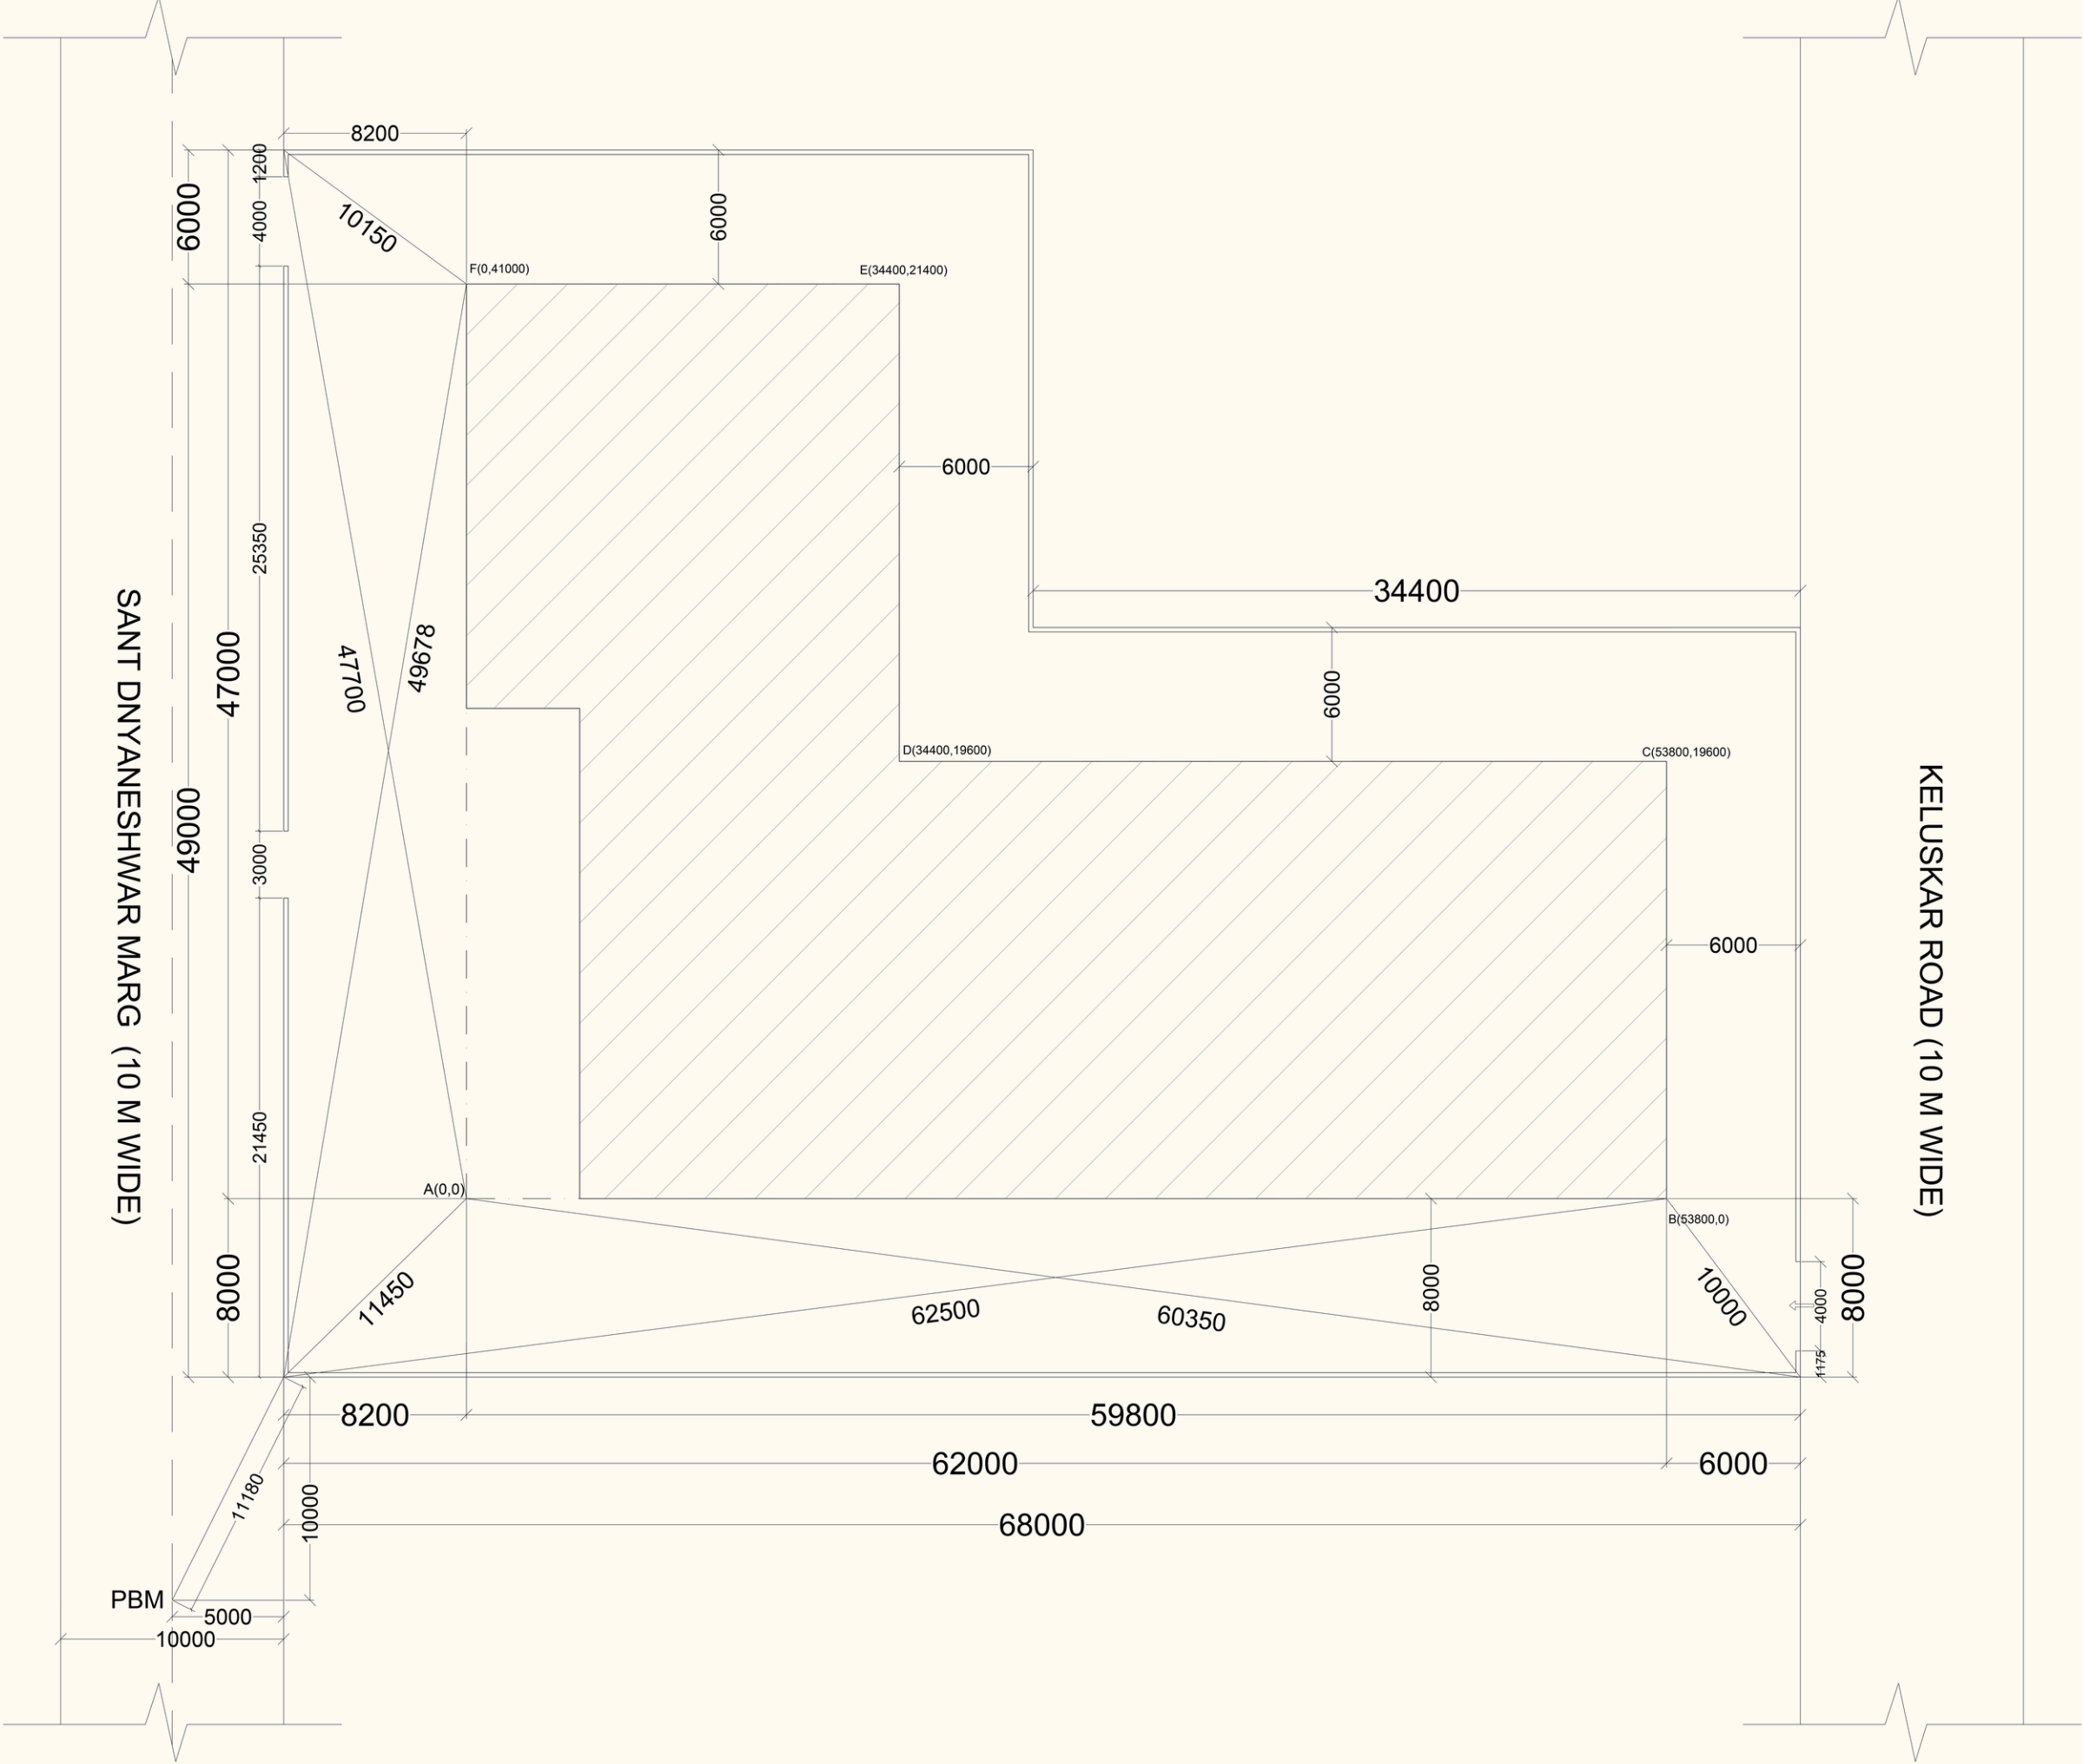

A			GENERAL NOTES		
1. ALL DIMENSIONS ARE IN MILLIMETERS (MM) UNLESS OTHERWISE SPECIFIED.					
2. DO NOT SCALE THE DRAWING. DIMENSIONS ARE TO BE READ AND NOT MEASURED.					
3. ALL LEVELS SHALL BE CROSS-CHECKED WITH THE ARCHITECT BEFORE COMMENCEMENT OF SITE WORK.					
4. ALL DIMENSIONS SHALL BE VERIFIED AT SITE PRIOR TO EXECUTION.					
5. ANY DISCREPANCY IN THE DRAWING SHALL BE BROUGHT TO THE NOTICE OF THE ARCHITECT BEFORE EXECUTION.					
6. FLOOR FINISH THICKNESS TO BE CONSIDERED AS 10 MM, UNLESS MENTIONED OTHERWISE.					
7. ALL FLOOR LEVELS INDICATED ARE FINISHED FLOOR LEVELS (FFL).					
8. INTERNAL PLASTER THICKNESS SHALL BE 12 MM AND EXTERNAL PLASTER THICKNESS SHALL BE 20 MM.					
9. FOR DOOR, WINDOW, AND OTHER FINISHES, REFER TO THE RESPECTIVE SCHEDULES.					
10. ALL STRUCTURAL DETAILS ARE SUGGESTIVE AND SHALL BE AS PER STRUCTURAL CONSULTANTS INPUTS.					
B			LEGEND		
		BUILDING PROFILE			
C			ABBREVIATIONS		
SP		STARTING POINT			
PBM		PERMANENT BENCH MARK			
D			CO-ORDINATES SCHEDULE		
SR. NO.		X- AXIS		Y- AXIS	
A		00		00	
B		53800		00	
C		53800		19600	
D		34400		19600	
E		34400		21400	
F		00		41000	

F KEY PLAN - (NTS)	

SETTING OUT PLAN

A GENERAL NOTES

1. ALL DIMENSIONS ARE IN MILLIMETERS (MM) UNLESS OTHERWISE SPECIFIED.
2. DO NOT SCALE THE DRAWING. DIMENSIONS ARE TO BE READ AND NOT MEASURED.
3. ALL LEVELS SHALL BE CROSS-CHECKED WITH THE ARCHITECT BEFORE COMMENCEMENT OF SITE WORK.
4. ALL DIMENSIONS SHALL BE VERIFIED AT SITE PRIOR TO EXECUTION.
5. ANY DISCREPANCY IN THE DRAWING SHALL BE BROUGHT TO THE NOTICE OF THE ARCHITECT BEFORE EXECUTION.
6. FLOOR FINISH THICKNESS TO BE CONSIDERED AS 10 MM, UNLESS MENTIONED OTHERWISE.
7. ALL FLOOR LEVELS INDICATED ARE FINISHED FLOOR LEVELS (FFL).
8. INTERNAL PLASTER THICKNESS SHALL BE 12 MM AND EXTERNAL PLASTER THICKNESS SHALL BE 20 MM.
9. FOR DOOR, WINDOW, AND OTHER FINISHES, REFER TO THE RESPECTIVE SCHEDULES.
10. ALL STRUCTURAL DETAILS ARE SUGGESTIVE AND SHALL BE AS PER STRUCTURAL CONSULTANTS INPUTS.

B LEGEND

	R.C.C. COLUMN
	SHEAR WALL
	200MM THK. EXTERNAL BRICK WORK
	150MM THK. INTRNL BRICK WORK
	SUNK SLAB
	FLOOR CUT OUT
	LEVEL DEFERENCE

C ABBREVIATIONS

C	COLUMN
S	SHEAR WALL
BSF	BUILDING STARTING FACE
BEF	BUILDING ENDING FACE


D COLUMN SCHEDULE

SR. NO.	SIZE X * Y	STRUCTURAL MEMBER
1	600 x 350	C1,C2,C5,C6,C7,C8,C9,C11,C12,C13,C16,C18,C19,C21,C29,C32
2	400 x 350	C3,C4,C14,C15,C22,C24,C26,C27,C28,C35,C36,C37,C38,C39,C40,C43
3	600 x 400	C10,C17,C20
4	700 x 350	C23,C31
5	850 x 350	C25,C30
6	900 x 350	C33
7	500 x 350	C34
8	400 x 400	C41,C42


E SHEAR WALL SCHEDULE


SHEAR WALL SIZES	SHEAR WALL NUMBERS
250x1850	SW1,SW3,
250x2400	SW2,SW4,
250x4250	SW5,SW8,SW10,SW13
250x2450	SW6,SW9,SW11,SW14
250x2000	SW7,SW12

F KEY PLAN - (NTS)

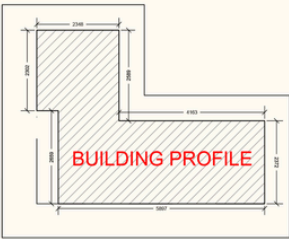

CENTRE LINE PLAN

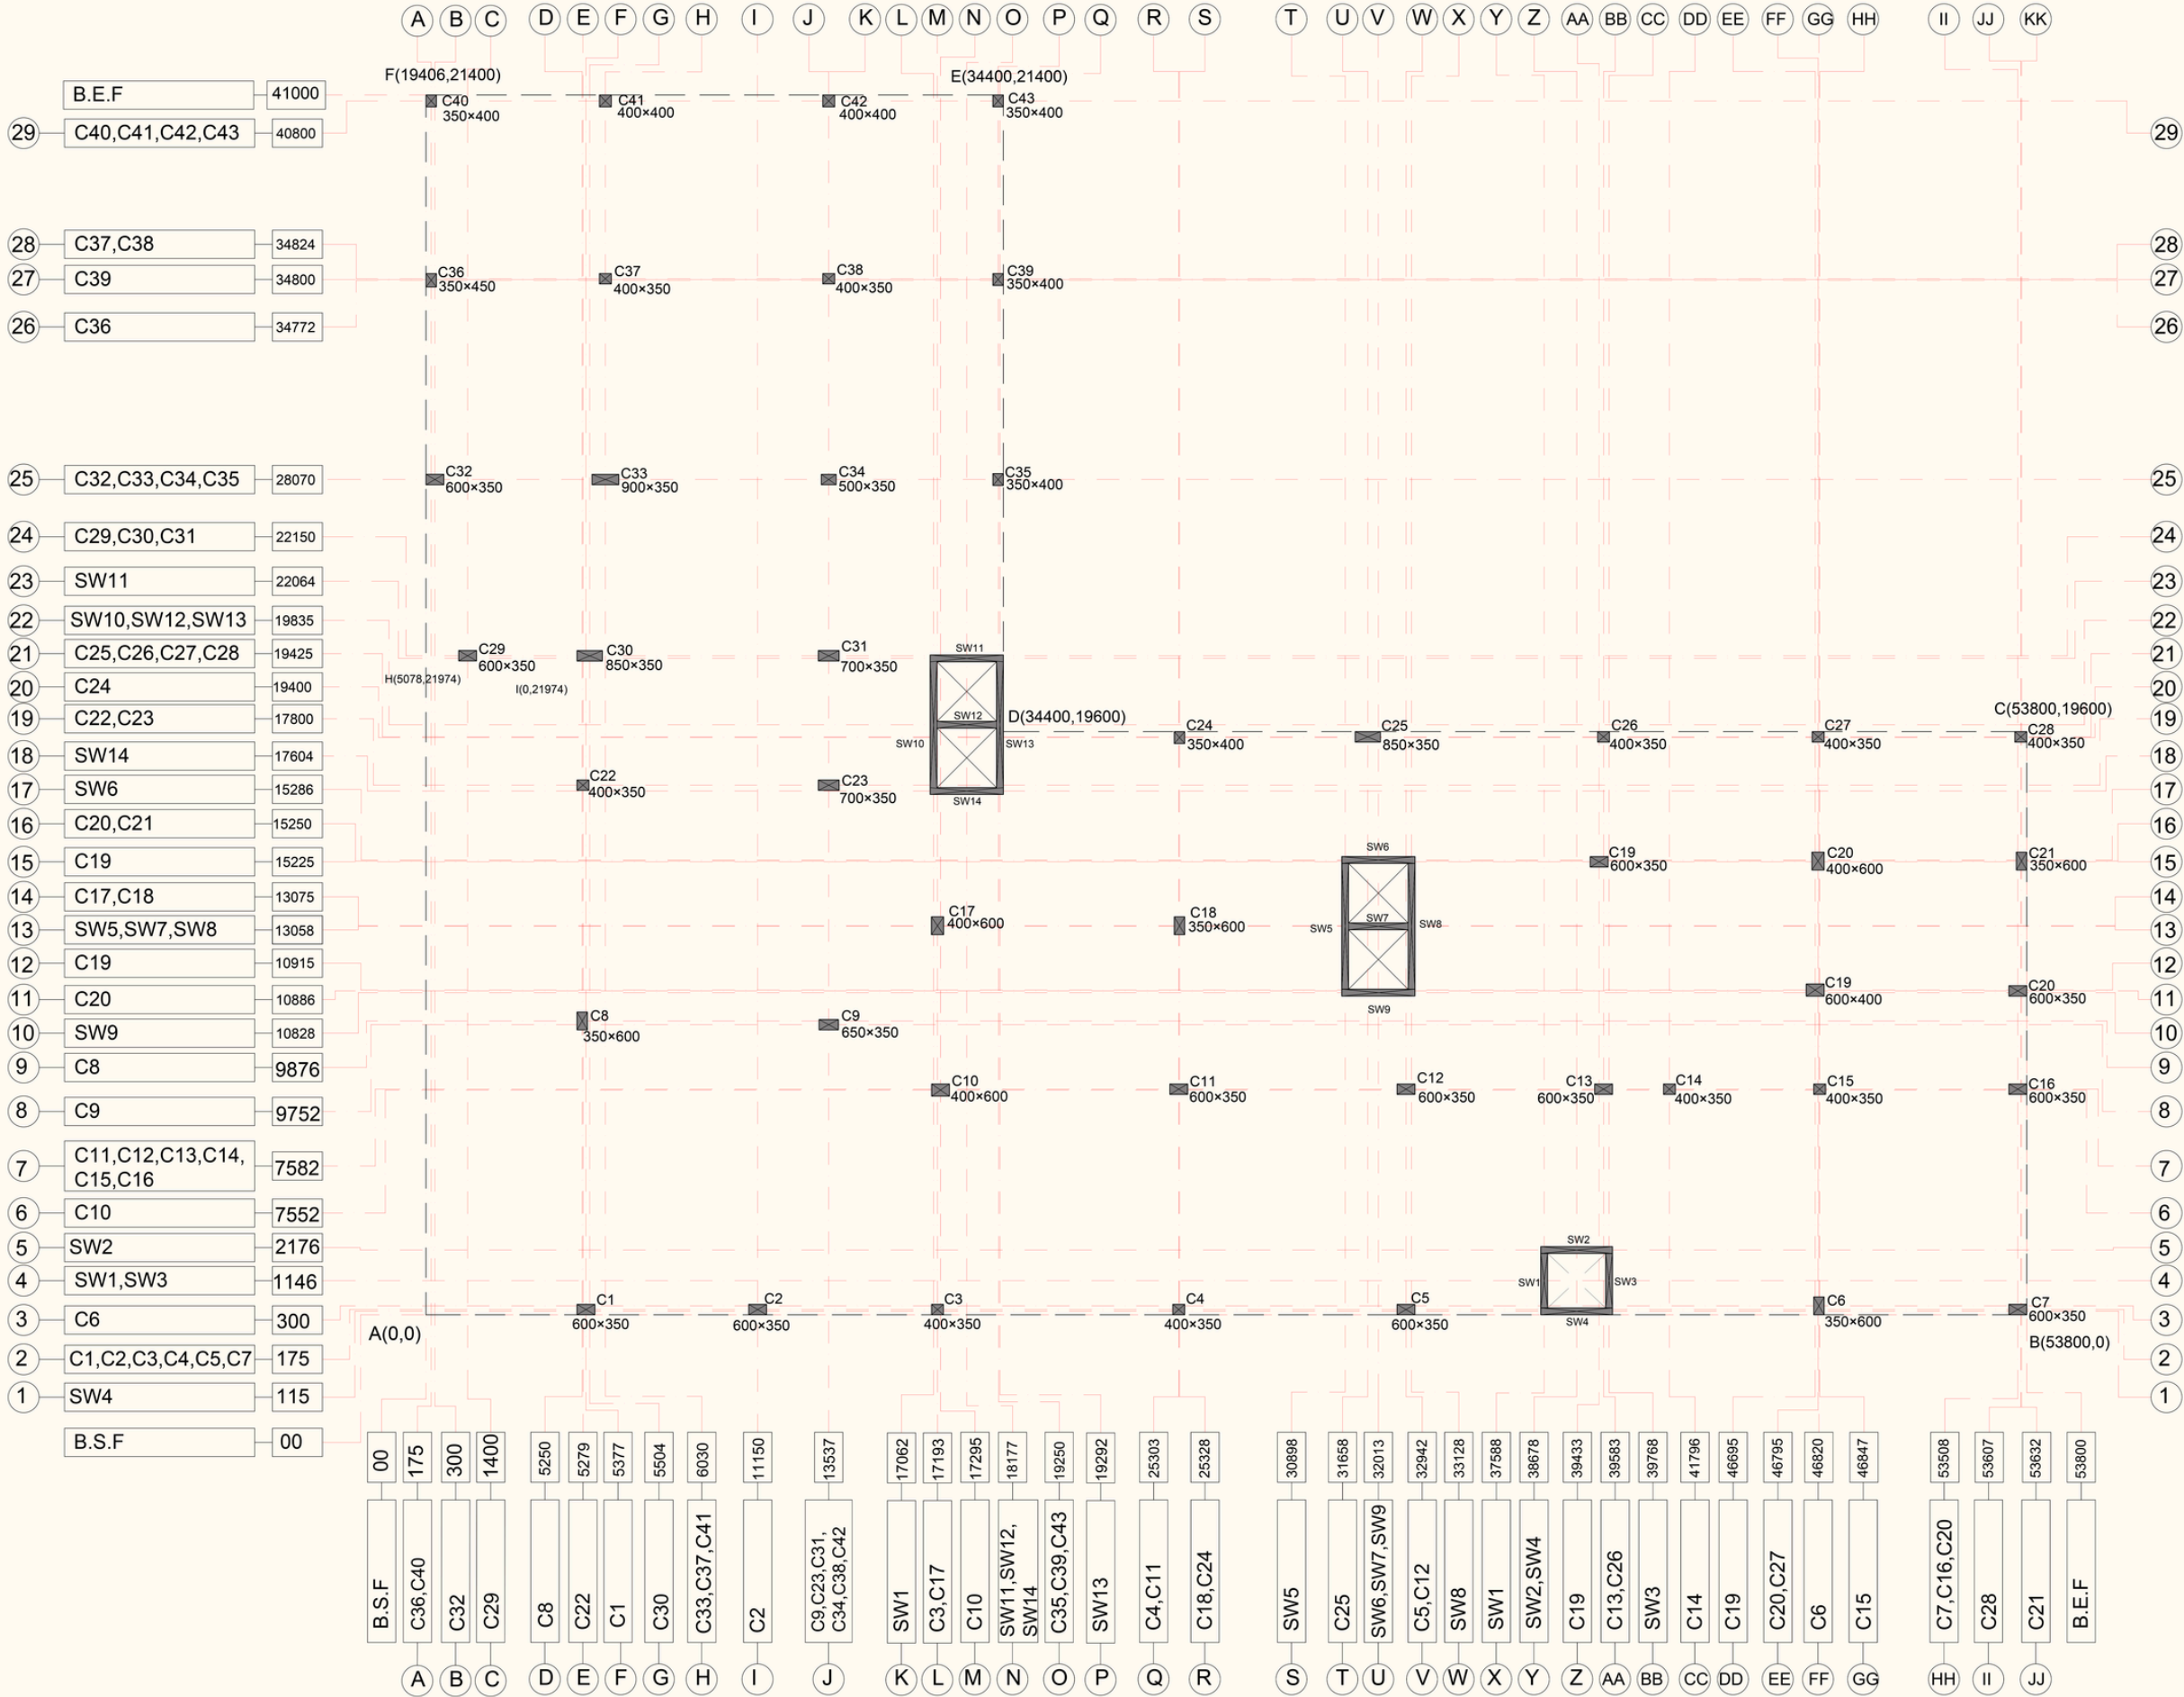

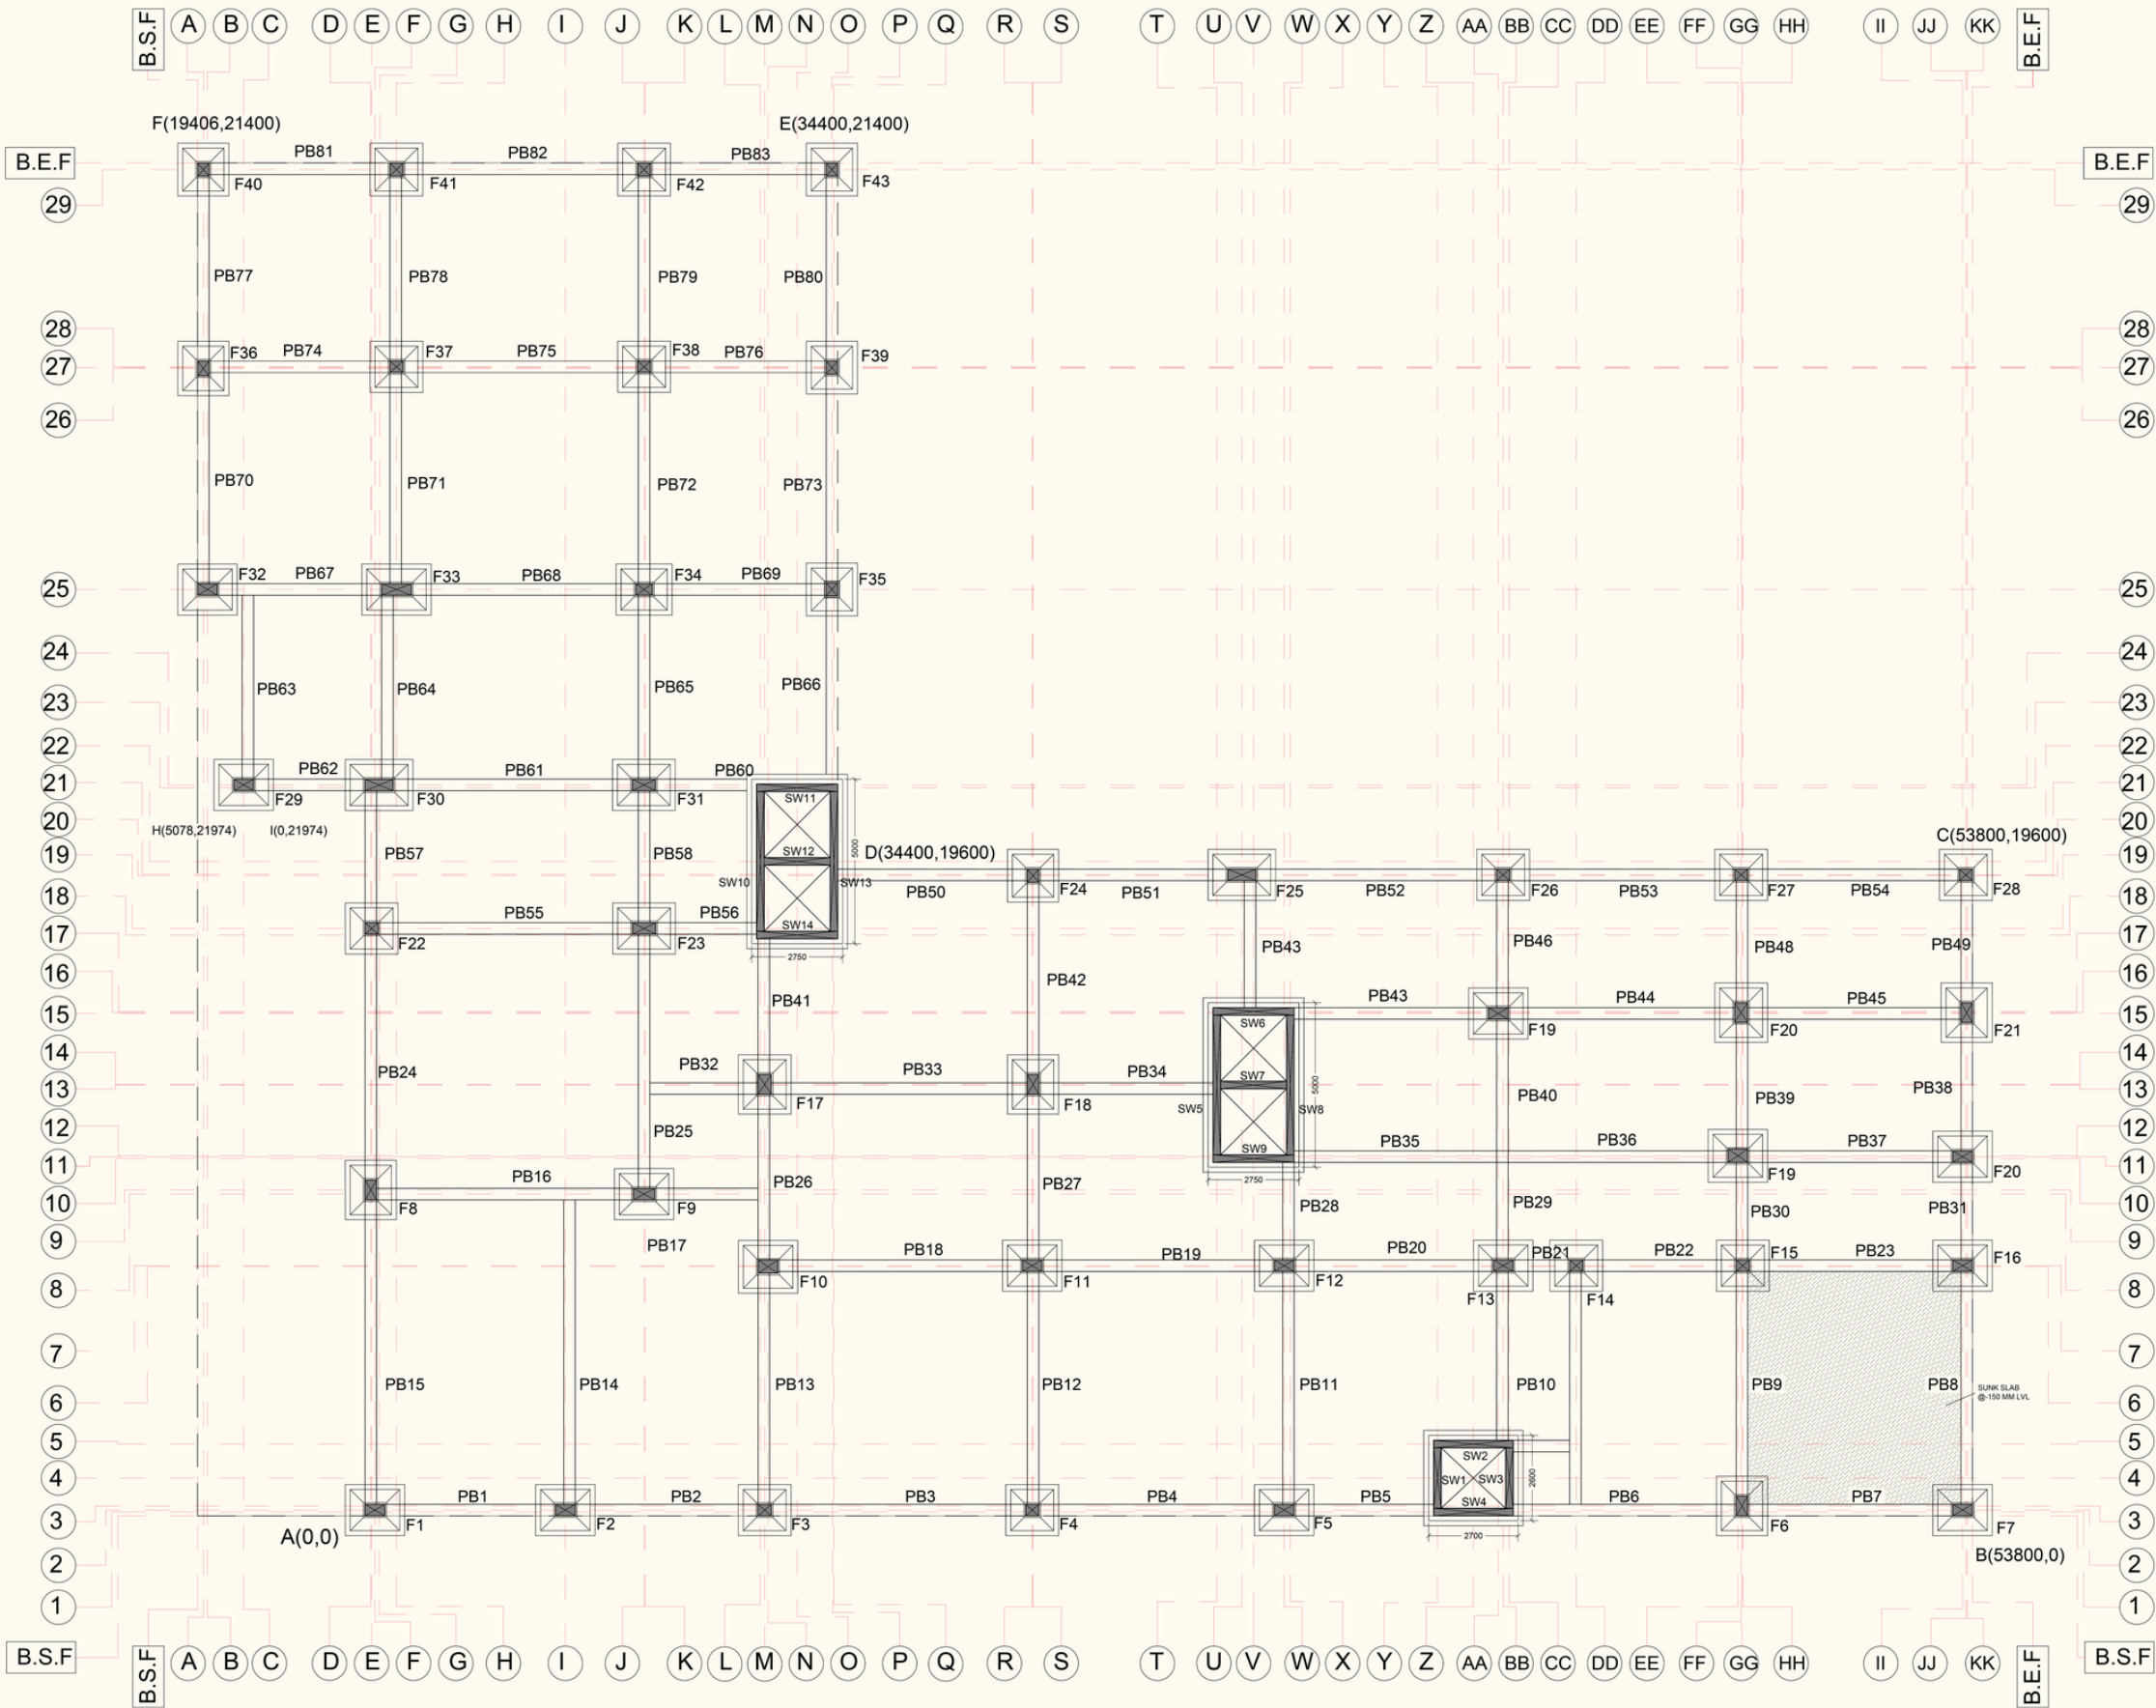

A GENERAL NOTES

1. ALL DIMENSIONS ARE IN MILLIMETERS (MM) UNLESS OTHERWISE SPECIFIED.
2. DO NOT SCALE THE DRAWING. DIMENSIONS ARE TO BE READ AND NOT MEASURED.
3. ALL LEVELS SHALL BE CROSS-CHECKED WITH THE ARCHITECT BEFORE COMMENCEMENT OF SITE WORK.
4. ALL DIMENSIONS SHALL BE VERIFIED AT SITE PRIOR TO EXECUTION.
5. ANY DISCREPANCY IN THE DRAWING SHALL BE BROUGHT TO THE NOTICE OF THE ARCHITECT BEFORE EXECUTION.
6. FLOOR FINISH THICKNESS TO BE CONSIDERED AS 10 MM, UNLESS MENTIONED OTHERWISE.
7. ALL FLOOR LEVELS INDICATED ARE FINISHED FLOOR LEVELS (FFL).
8. INTERNAL PLASTER THICKNESS SHALL BE 12 MM AND EXTERNAL PLASTER THICKNESS SHALL BE 20 MM.
9. FOR DOOR, WINDOW, AND OTHER FINISHES, REFER TO THE RESPECTIVE SCHEDULES.
10. ALL STRUCTURAL DETAILS ARE SUGGESTIVE AND SHALL BE AS PER STRUCTURAL CONSULTANTS INPUTS.

B LEGEND

	R.C.C. COLUMN
	SHEAR WALL
	CENTER LINE
	HIDDEN FOOTING LINE
	SUNK SLAB

C ABBREVIATIONS

SP	STARTING POINT
PB	PLINTH BEAM
F	FOOTING
SW	SHEAR WALL

D FOUNDATION SCHEDULE

SR. NO.	SIZE X * Y	STRUCTURAL MEMBER
1	1800x 1550	F1,F2,F5,F6,F7,F8,F9,F11, F12,F13,F16,F18,F19,F21, F29,F32
2	1600x 1550	F3,F4,F14,F15,F22,F24, F26,F27,F28,F35,F36,F37, F38,F39,F40,F43
3	1800x 1600	F10,F17,F20
4	1900x 1550	F23,F31
5	2050x 1550	F25,F30
6	2100x 1550	F33
7	1700x 1550	F34
8	1600x 1600	F41,F42


E PLINTH BEAM SCHEDULE

NO.	SIZE X*Y	STRUCTURAL MEMBER
1.	350x350	PB1 TO PB83

F SHEAR WALL SCHEDULE

SHEAR WALL SIZES	SHEAR WALL NUMBERS
250x1850	SW1,SW3,
250x2400	SW2,SW4,
250x4250	SW5,SW8,SW10,SW13
250x2450	SW6,SW9,SW11,SW14
250x2000	SW7,SW12

F KEY PLAN - (NTS)

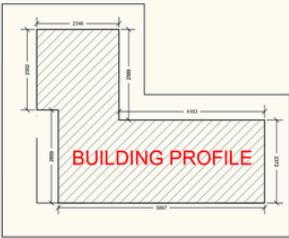

PLINTH-BEAM PLAN


VEHICULAR
ENTRY
ϕ +0.00M

PEDESTRIAN
ENTRY
ϕ +0.00M

A'

B

SERVICE
ENTRY
ϕ +0.00M

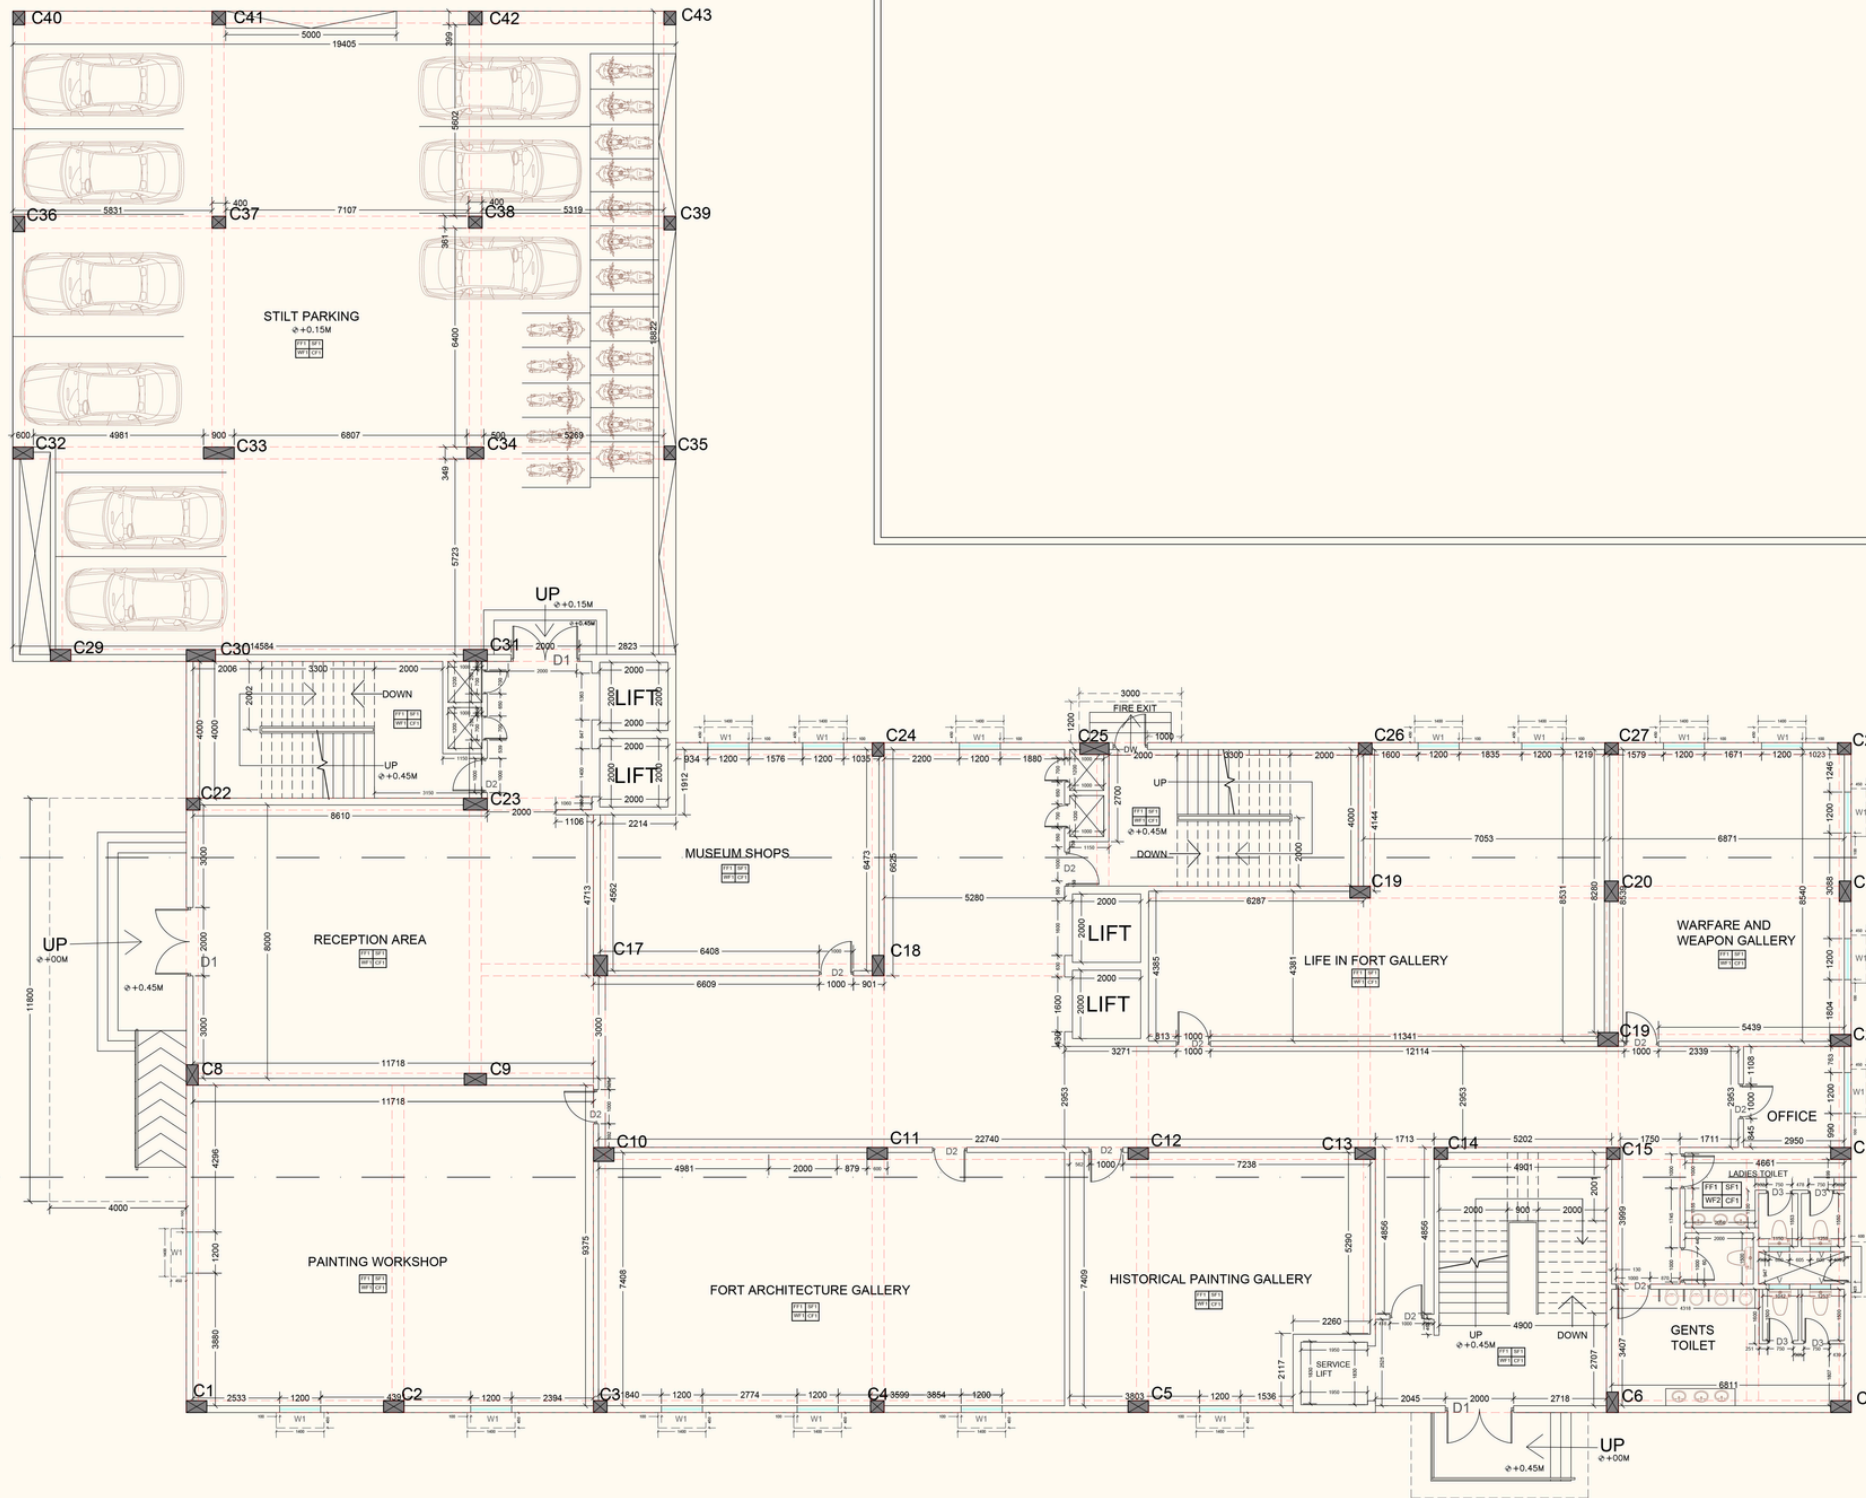

A GENERAL NOTES

1. ALL DIMENSIONS ARE IN MILLIMETERS (MM) UNLESS OTHERWISE SPECIFIED.
2. DO NOT SCALE THE DRAWING. DIMENSIONS ARE TO BE READ AND NOT MEASURED.
3. ALL LEVELS SHALL BE CROSS-CHECKED WITH THE ARCHITECT BEFORE COMMENCEMENT OF SITE WORK.
4. ALL DIMENSIONS SHALL BE VERIFIED AT SITE PRIOR TO EXECUTION.
5. ANY DISCREPANCY IN THE DRAWING SHALL BE BROUGHT TO THE NOTICE OF THE ARCHITECT BEFORE EXECUTION.
6. FLOOR FINISH THICKNESS TO BE CONSIDERED AS 10 MM, UNLESS MENTIONED OTHERWISE.
7. ALL FLOOR LEVELS INDICATED ARE FINISHED FLOOR LEVELS (FFL).
8. INTERNAL PLASTER THICKNESS SHALL BE 12 MM AND EXTERNAL PLASTER THICKNESS SHALL BE 20 MM.
9. FOR DOOR, WINDOW, AND OTHER FINISHES, REFER TO THE RESPECTIVE SCHEDULES.
10. ALL STRUCTURAL DETAILS ARE SUGGESTIVE AND SHALL BE AS PER STRUCTURAL CONSULTANTS INPUTS.

B LEGEND

	R.C.C. COLUMN
	SHEAR WALL
	200MM THK. EXTERNAL BRICK WORK
	150MM THK. INTRNAL BRICK WORK
	SUNK SLAB
	FLOOR CUT OUT
	LEVEL DEFERENCE

C ABBREVIATIONS

FF	FLOOR FINISH
SF	SKIRTING FINISH
WF	WALL FINISH
CF	CEILING FINISH
C	COLUMN
D	DOOR
W	WINDOW


D DOOR & WINDOW SCHEDULE

Type	Size	Sill lvl.	Lintel Lvl.	Specification
D1	2000	-	2100	DOUBLE HINGED
D2	1000	-	2100	SINGLE HINGED
D3	750	-	2100	SINGLE HINGED
W1	1200	900	2100	DOUBLE HINGED
V1	600	1500	2100	SINGLE HINGED


E FINISHES SCHEDULE

W=WALL	F=FLOOR	C=CEILING	S=SKIRTING
FF1	VITRIFIED TILES		
WF1	GYPSUM PLASTERED FINISH WITH ACRYLIC EMULSION PAINT		
WF2	MATT FINISHED CERAMIC TILES DADO 2100MM HIGH		
SF1	VITRIFIED TILES		
CF1	SUSPENDED FALSE CEILING		

F KEY PLAN - (NTS)

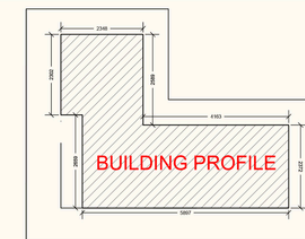

GROUND FLOOR PLAN

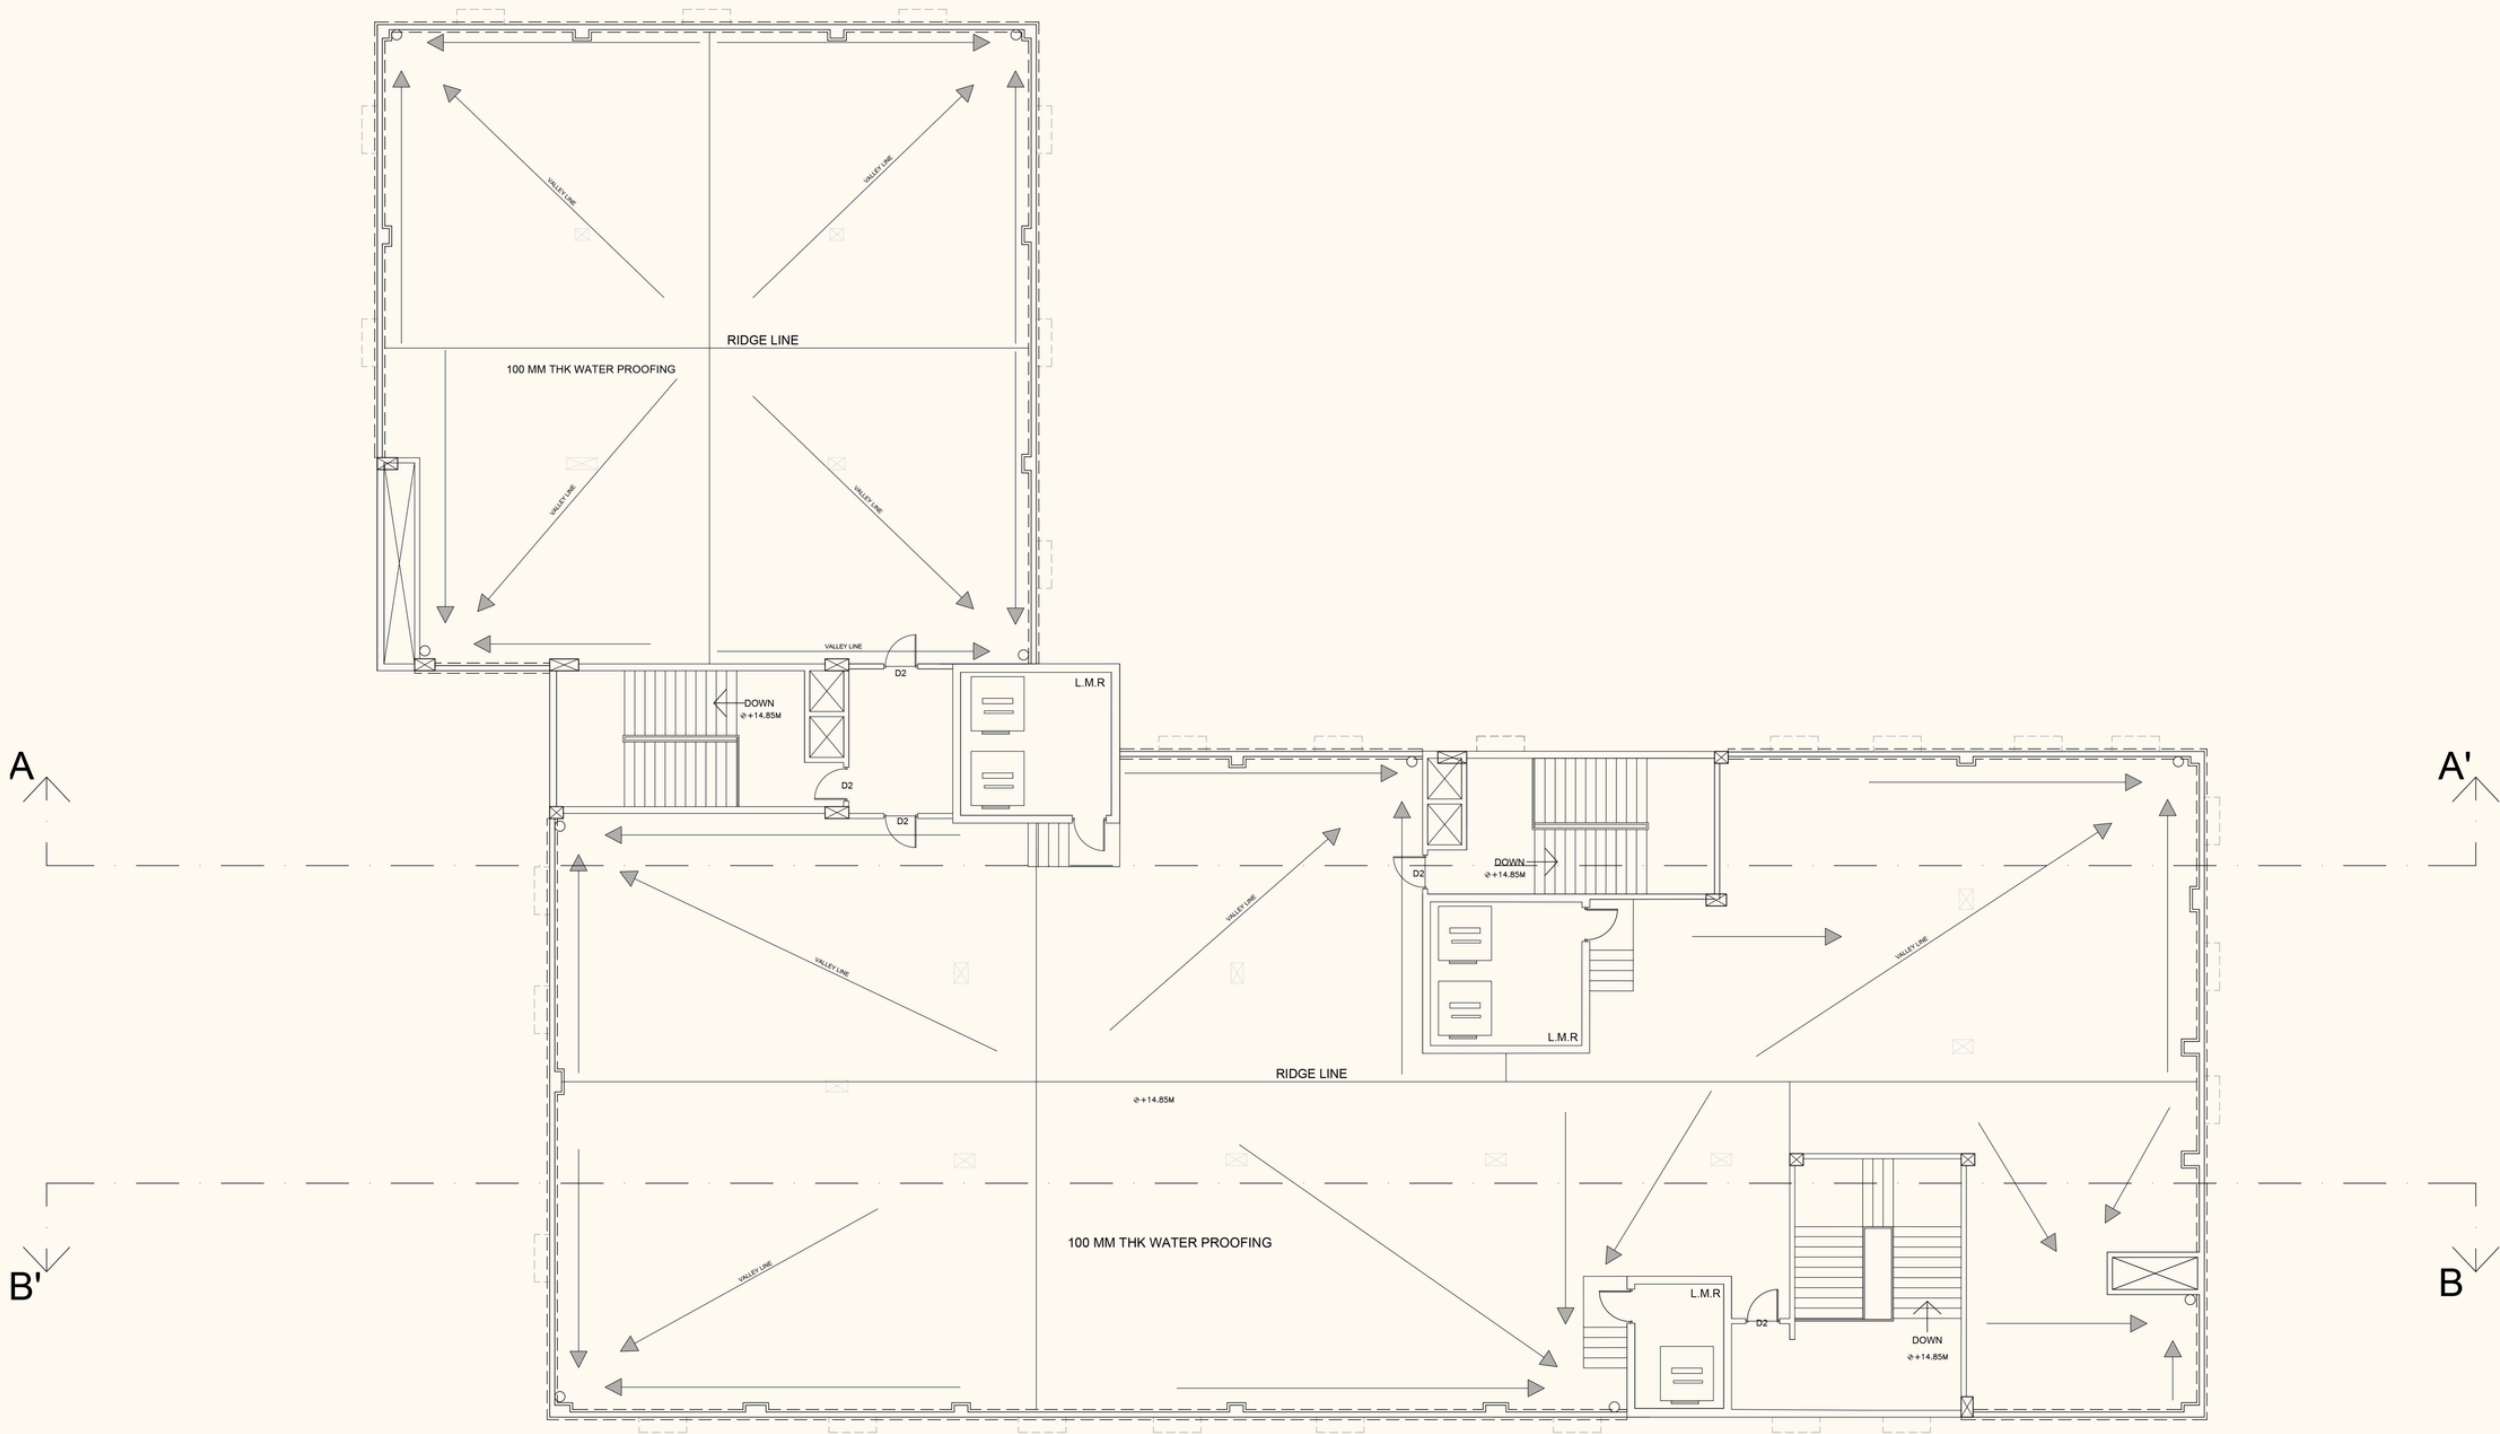

A GENERAL NOTES

- 1. ALL DIMENSIONS ARE IN MILLIMETERS (MM) UNLESS OTHERWISE SPECIFIED.
- 2. DO NOT SCALE THE DRAWING. DIMENSIONS ARE TO BE READ AND NOT MEASURED.
- 3. ALL LEVELS SHALL BE CROSS-CHECKED WITH THE ARCHITECT BEFORE COMMENCEMENT OF SITE WORK.
- 4. ALL DIMENSIONS SHALL BE VERIFIED AT SITE PRIOR TO EXECUTION.
- 5. ANY DISCREPANCY IN THE DRAWING SHALL BE BROUGHT TO THE NOTICE OF THE ARCHITECT BEFORE EXECUTION.
- 6. FLOOR FINISH THICKNESS TO BE CONSIDERED AS 10 MM, UNLESS MENTIONED OTHERWISE.
- 7. ALL FLOOR LEVELS INDICATED ARE FINISHED FLOOR LEVELS (FFL).
- 8. INTERNAL PLASTER THICKNESS SHALL BE 12 MM AND EXTERNAL PLASTER THICKNESS SHALL BE 20 MM.
- 9. FOR DOOR, WINDOW, AND OTHER FINISHES, REFER TO THE RESPECTIVE SCHEDULES.
- 10. ALL STRUCTURAL DETAILS ARE SUGGESTIVE AND SHALL BE AS PER STRUCTURAL CONSULTANTS INPUTS.

B LEGEND

	R.C.C. COLUMN
	SHEAR WALL
	200MM THK. EXTERNAL BRICK WORK
	150MM THK. INTRNAL BRICK WORK
	SUNK SLAB
	FLOOR CUT OUT
	LEVEL DEFERENCE

C ABBREVIATIONS

FF	FLOOR FINISH
SF	SKIRTING FINISH
WF	WALL FINISH
CF	CEILING FINISH
C	COLUMN
D	DOOR
W	WINDOW


D DOOR & WINDOW SCHEDULE

Type	Size	Sill lvl.	Lintel Lvl.	Specification
D1	2000	-	2100	DOUBLE HINGED
D2	1000	-	2100	SINGLE HINGED
D3	750	-	2100	SINGLE HINGED
W1	1200	900	2100	DOUBLE HINGED
V1	600	1500	2100	SINGLE HINGED

E FINISHES SCHEDULE

W=WALL	F =FLOOR	C =CEILING	S =SKIRTING
FF1	VITRIFIED TILES		
WF1	GYPSUM PLASTERED FINISH WITH ACRYLIC EMULSION PAINT		
WF2	MATT FINISHED CERAMIC TILES DADO 2100MM HIGH		
SF1	VITRIFIED TILES		
CF1	SUSPENDED FALSE CEILING		

F KEY PLAN - (NTS)

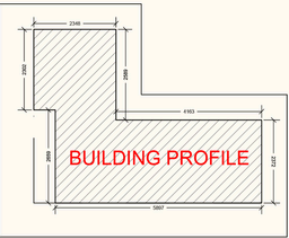

TERRACE PLAN

A GENERAL NOTES

1. ALL DIMENSIONS ARE IN MILLIMETERS (MM) UNLESS OTHERWISE SPECIFIED.
2. DO NOT SCALE THE DRAWING. DIMENSIONS ARE TO BE READ AND NOT MEASURED.
3. ALL LEVELS SHALL BE CROSS-CHECKED WITH THE ARCHITECT BEFORE COMMENCEMENT OF SITE WORK.
4. ALL DIMENSIONS SHALL BE VERIFIED AT SITE PRIOR TO EXECUTION.
5. ANY DISCREPANCY IN THE DRAWING SHALL BE BROUGHT TO THE NOTICE OF THE ARCHITECT BEFORE EXECUTION.
6. FLOOR FINISH THICKNESS TO BE CONSIDERED AS 10 MM, UNLESS MENTIONED OTHERWISE.
7. ALL FLOOR LEVELS INDICATED ARE FINISHED FLOOR LEVELS (FFL).
8. INTERNAL PLASTER THICKNESS SHALL BE 12 MM AND EXTERNAL PLASTER THICKNESS SHALL BE 20 MM.
9. FOR DOOR, WINDOW, AND OTHER FINISHES, REFER TO THE RESPECTIVE SCHEDULES.
10. ALL STRUCTURAL DETAILS ARE SUGGESTIVE AND SHALL BE AS PER STRUCTURAL CONSULTANTS INPUTS.

B LEGEND

	R.C.C. COLUMN
	SHEAR WALL
	200MM THK. EXTERNAL BRICK WORK
	150MM THK. INTRNAL BRICK WORK
	SUNK SLAB
	FLOOR CUT OUT
	LEVEL DEFERENCE

C ABBREVIATIONS

FF	FLOOR FINISH
SF	SKIRTING FINISH
WF	WALL FINISH
CF	CEILING FINISH
C	COLUMN
D	DOOR
W	WINDOW



D DOOR & WINDOW SCHEDULE

Type	Size	Sill lvl.	Lintel Lvl.	Specification
D1	2000	-	2100	DOUBLE HINGED
D2	1000	-	2100	SINGLE HINGED
D3	750	-	2100	SINGLE HINGED
W1	1200	900	2100	DOUBLE HINGED
V1	600	1500	2100	SINGLE HINGED


E FINISHES SCHEDULE

W=WALL	F =FLOOR	C =CEILING	S =SKIRTING
FF1	VITRIFIED TILES		
WF1	GYPSUM PLASTERED FINISH WITH ACRYLIC EMULSION PAINT		
WF2	MATT FINISHED CERAMIC TILES DADO 2100MM HIGH		
SF1	VITRIFIED TILES		
CF1	SUSPENDED FALSE CEILING		

F KEY PLAN - (NTS)

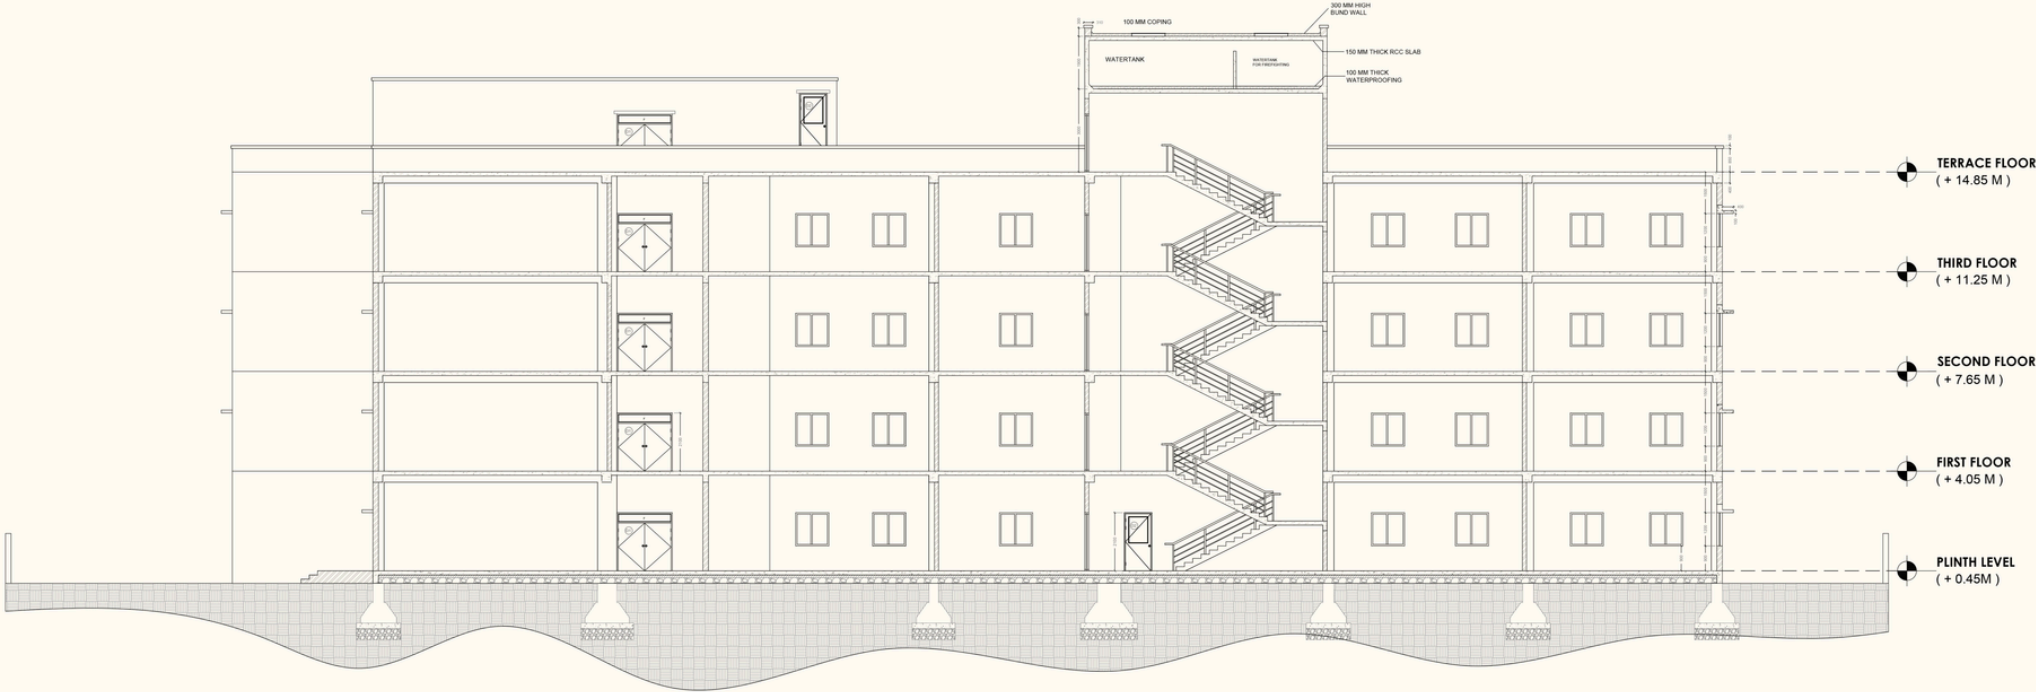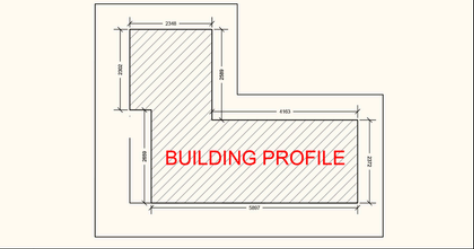


SECTION AA'

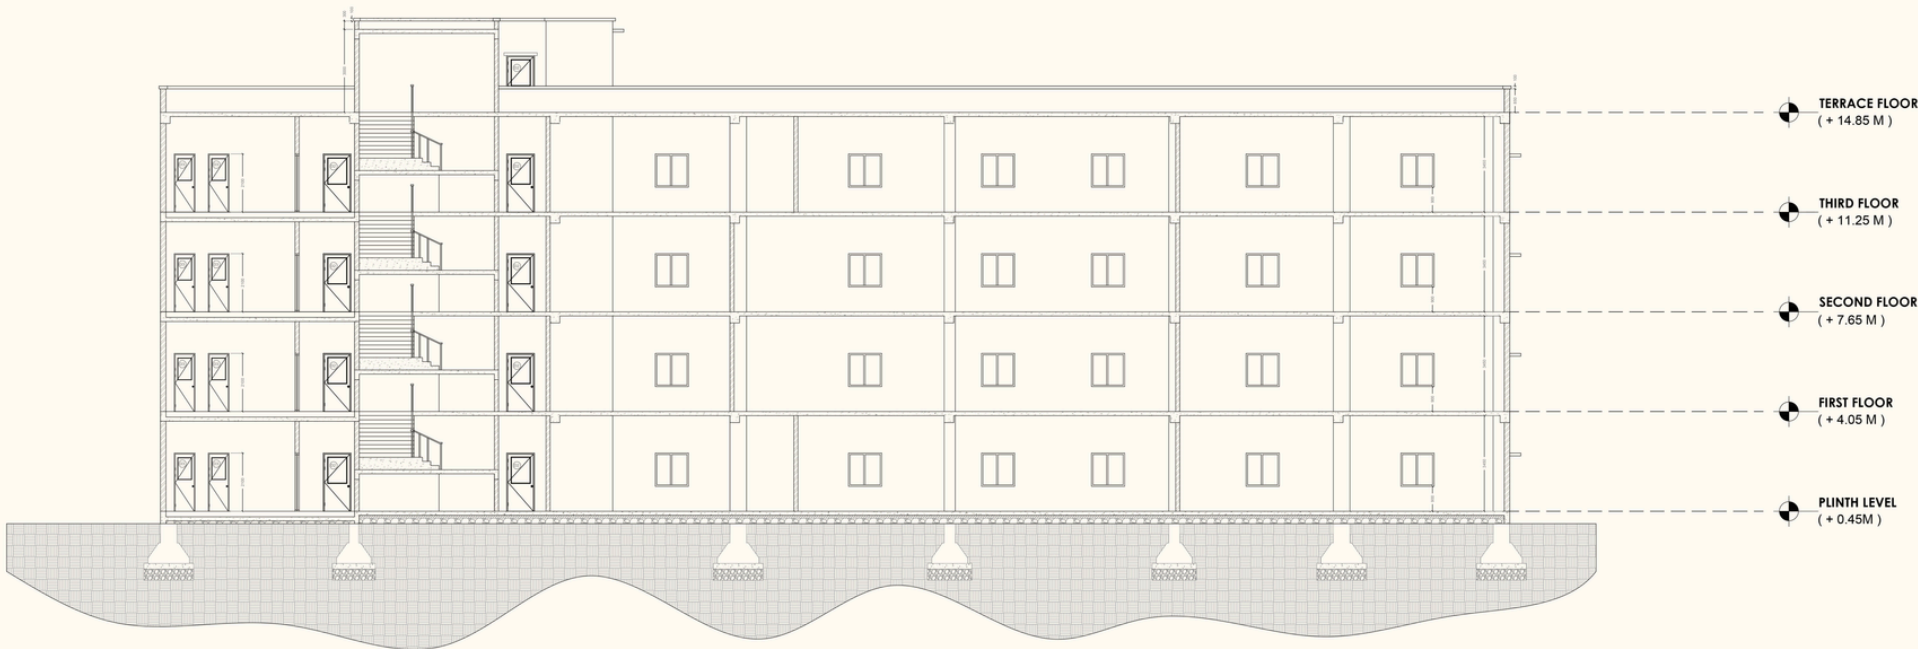


SECTION BB'

A GENERAL NOTES







1. ALL DIMENSIONS ARE IN MILLIMETERS (MM) UNLESS OTHERWISE

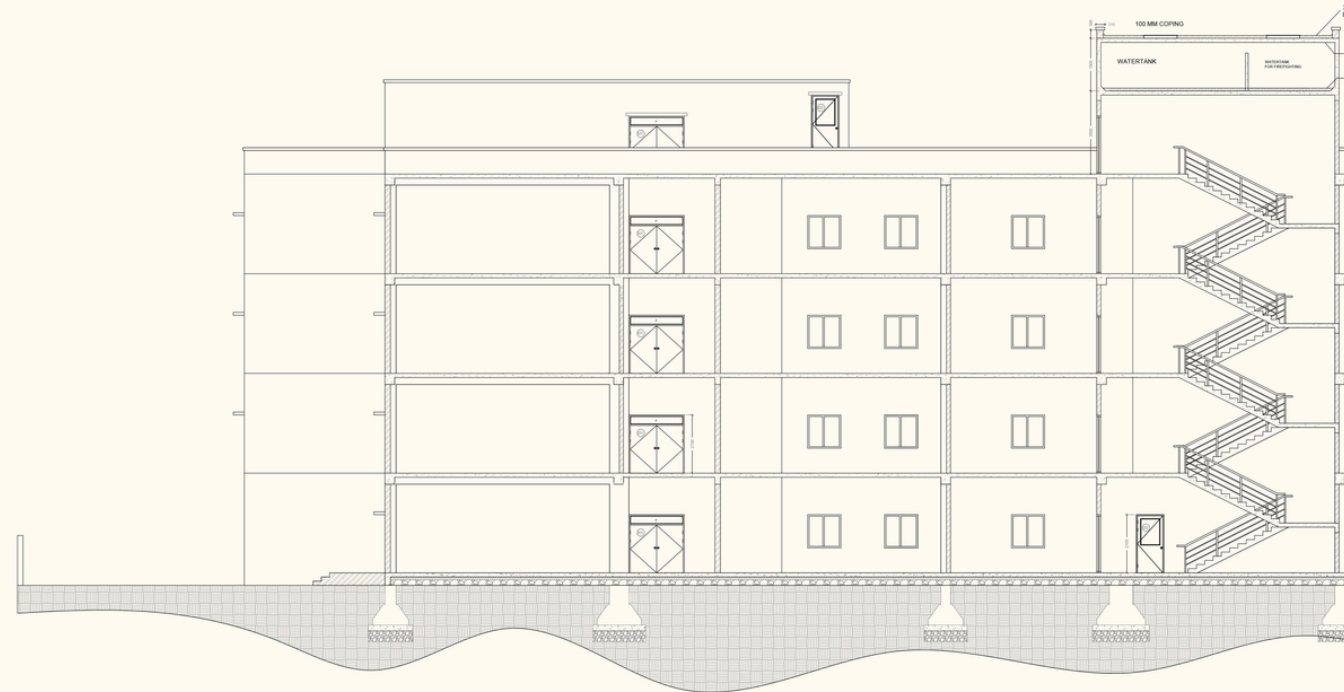


SECTION AA'

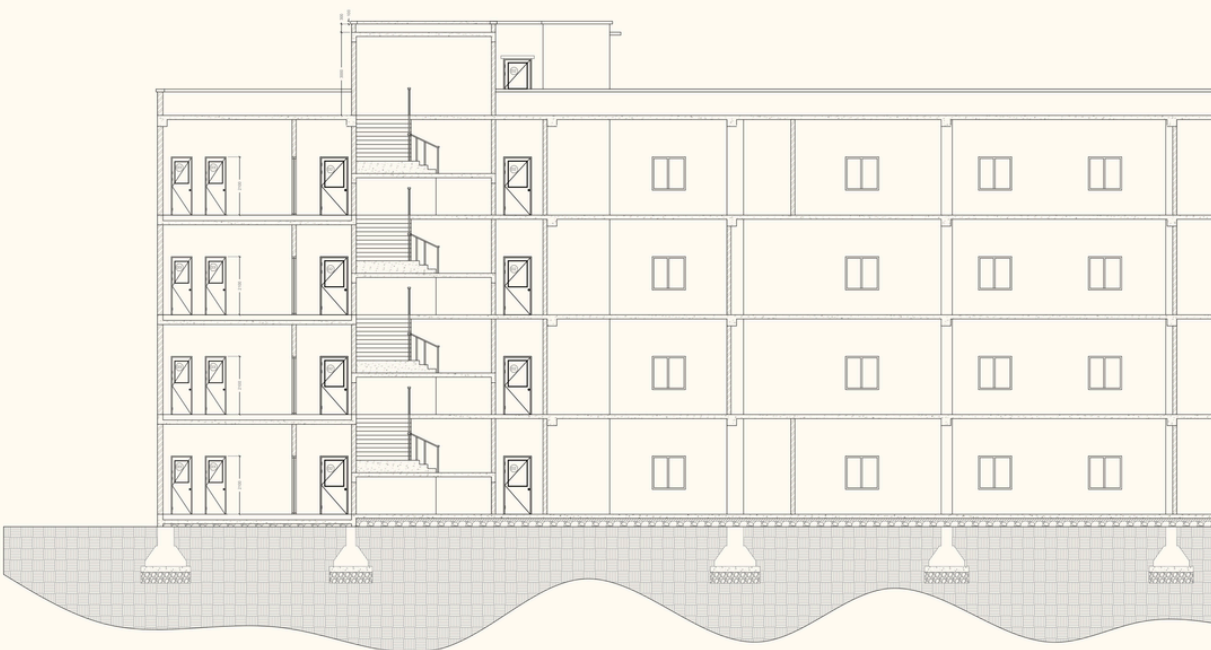

SECTION BB'

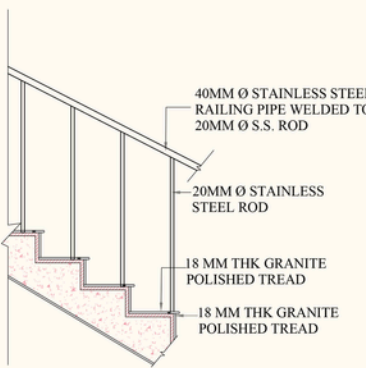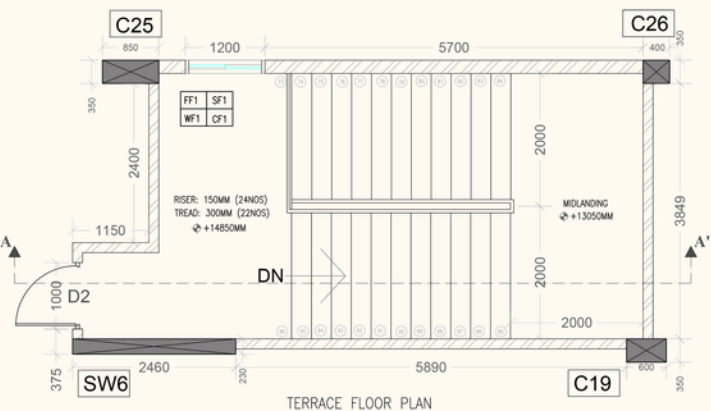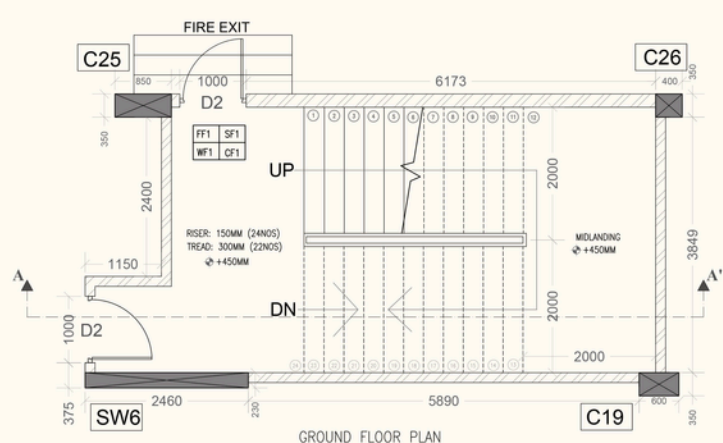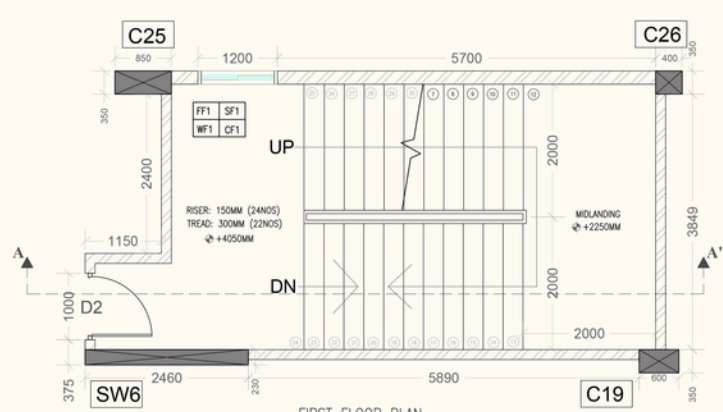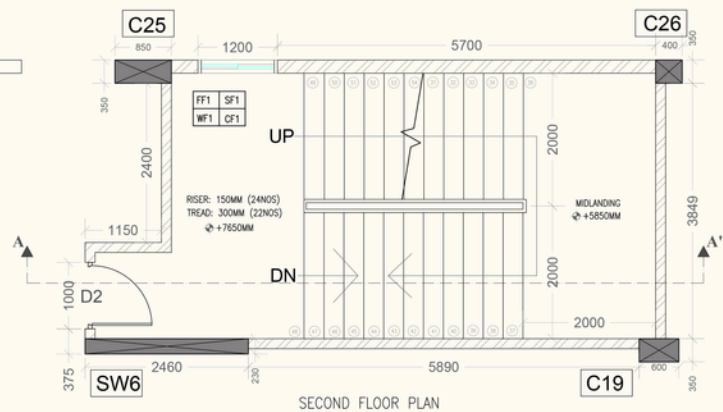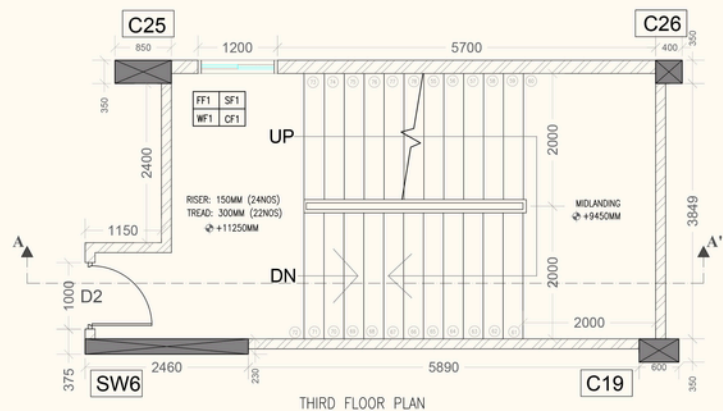

TYPICAL RAILING DETAIL
SCALE - 1:20

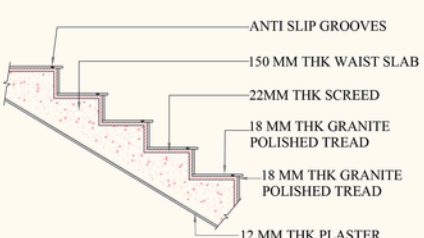

TYPICAL TREAD AND
RISER DETAIL
SCALE - 1:20

